

PLANTA DO TÉRREO

esc. 1:100

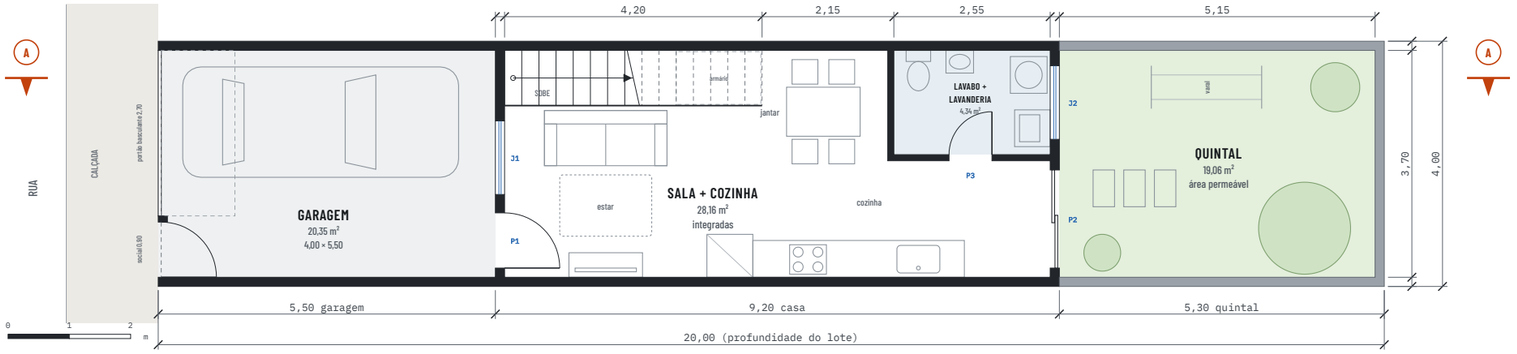


PLANTA DO PAVIMENTO SUPERIOR

esc. 1:100

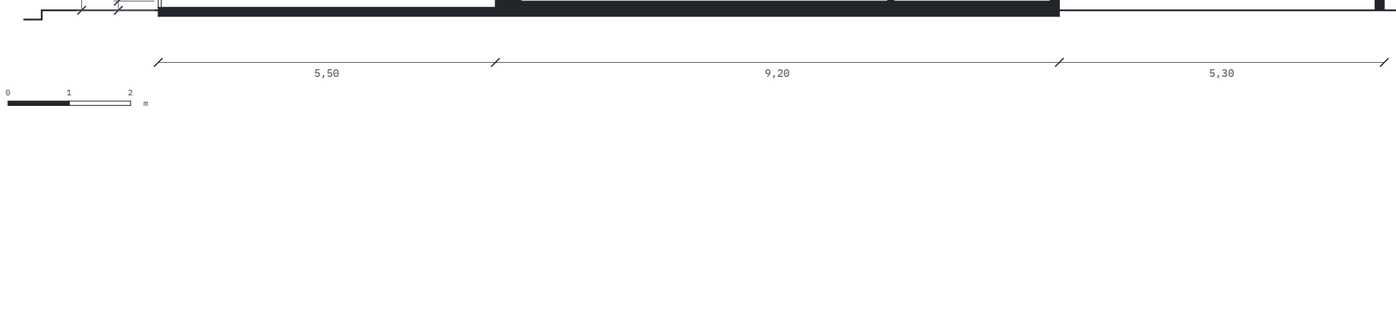


CORTE AA

esc. 1:100

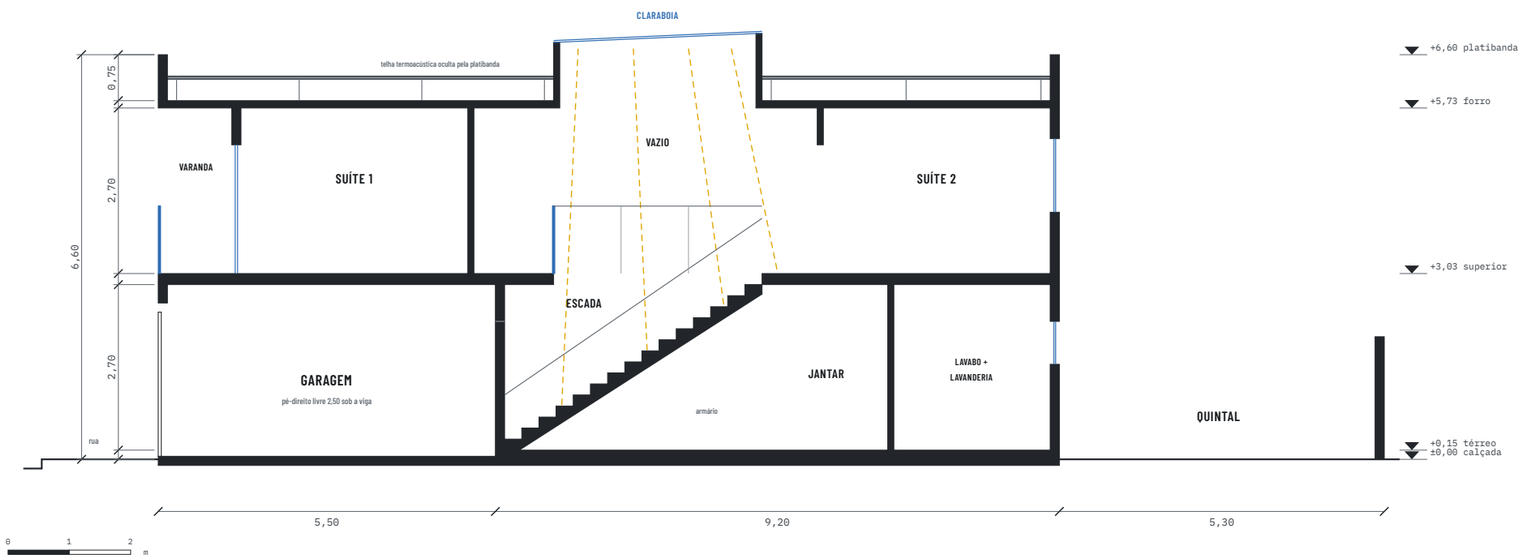

FACHADA FRONTAL

esc. 1:100

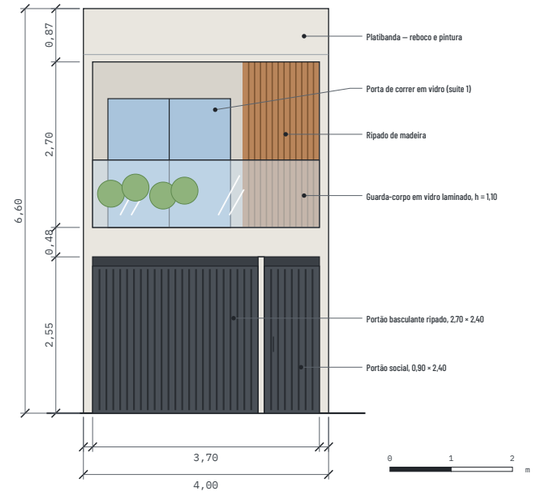

QUADRO DE ÁREAS (M²)

Garagem (coberta)	20,35
Sala + cozinha integradas (inclui escada)	28,16
Lavabo + lavanderia	4,34
Varanda	4,44
Suíte 1 (quarto)	13,69
Banho suíte 1	4,95
Circulação	7,02
Banho suíte 2	4,95
Suíte 2 (quarto)	13,69
Quintal descoberto	19,06
Área construída total (térreo 58,80 + superior 58,80)	**117,60**
Taxa de ocupação · Coef. aproveitamento · Permeável	73,5% · 1,47 · 23,8%

QUADRO DE ESQUADRIAS

CÓD.	TIPO	L × H	PEIT.	QTD
P1	Porta de entrada, de giro	0,90 × 2,10	—	1
P2	Porta de correr de vidro, 2 folhas	1,60 × 2,10	—	1
P3	Porta de giro	0,70 × 2,10	—	1
P4	Porta de correr de vidro, 2 folhas	2,00 × 2,10	—	1
P5	Porta de giro	0,80 × 2,10	—	2
P6	Porta de giro	0,70 × 2,10	—	2
J1	Janela de correr	1,20 × 1,20	1,00	1
J2	Janela basculante	1,20 × 0,70	1,40	1
J3	Janela de correr	2,00 × 1,20	1,00	1
PG	Portão basculante ripado	2,70 × 2,40	—	1
PS	Portão social ripado	0,90 × 2,40	—	1

Escada: 16 espelhos de 18 cm, pisos de 28 cm, largura 0,90 m, guarda-corpo h = 1,10 m. Pé-direito 2,70 m. Paredes laterais cegas (Código Civil, art. 1.301). Banheiros do superior com exaustão mecânica até a cobertura. Verificar recuos e índices no código de obras e no zoneamento do município.

PROJETO

Sobrado 4×20 — anteprojeto

LOTE	ÁREA CONSTRUÍDA
4,00 × 20,00 m (80,00 m²)	**117,60 m²**
ESCALA	DATA
1:100 (A3)	**nov/2026**

OBSERVAÇÃO

Estudo preliminar. Não substitui o projeto legal assinado por responsável técnico (RRT/ART).