

PLANTA BAIXA

esc. 1:100

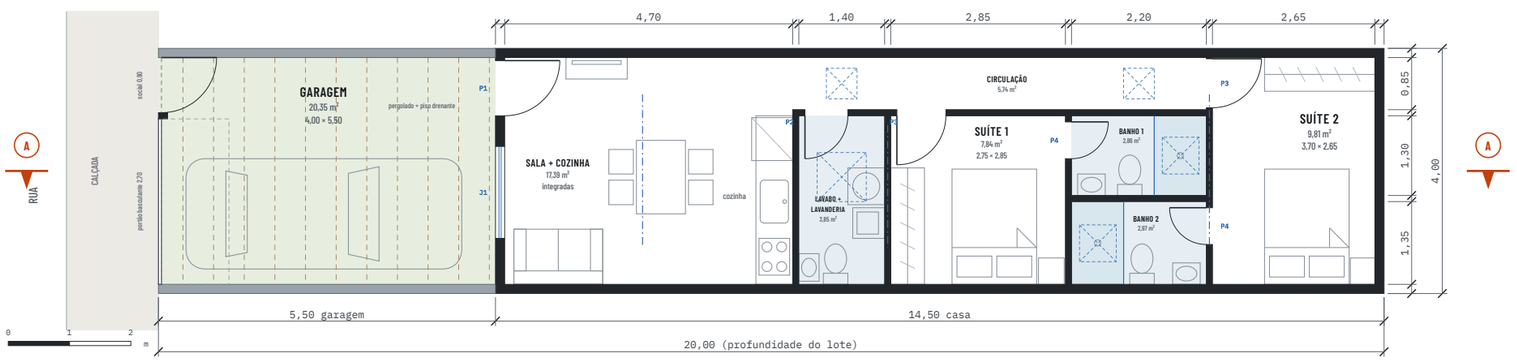


FACHADA FRONTAL

esc. 1:100

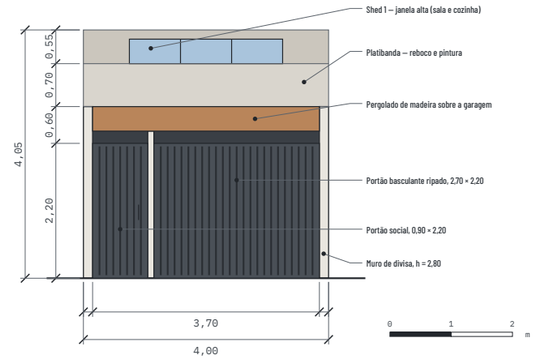


PLANTA DE COBERTURA

esc. 1:100

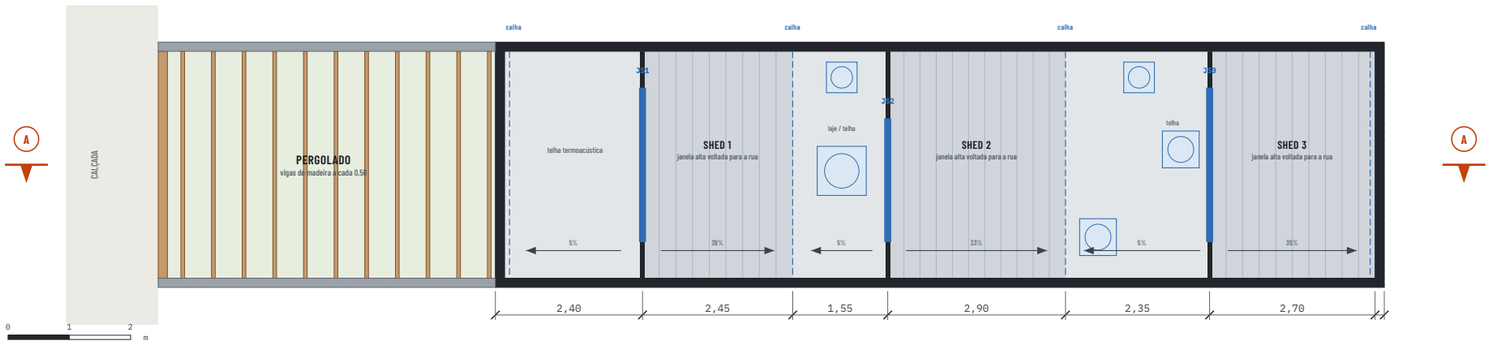

CORTE AA

esc. 1:100

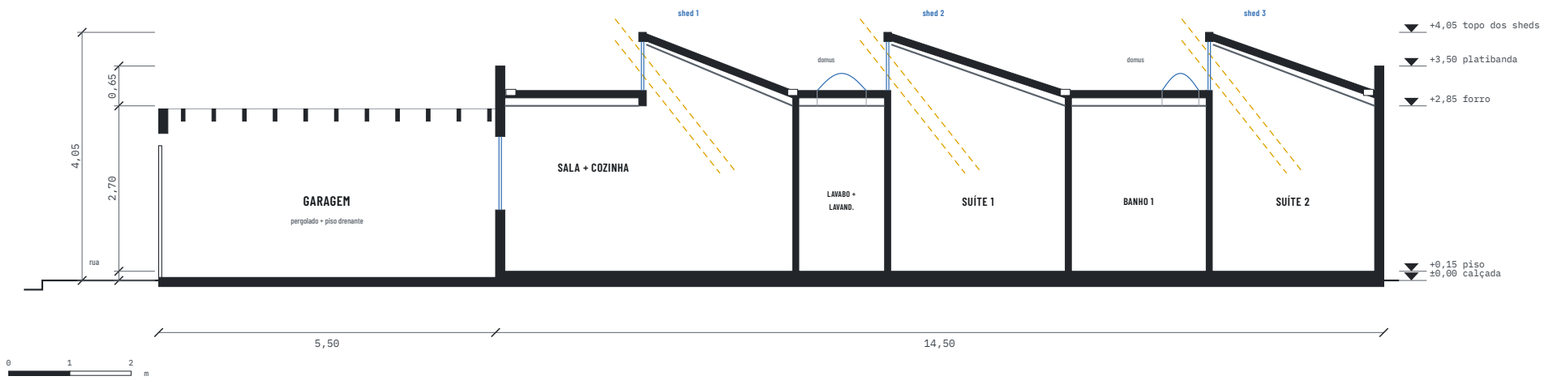

QUADRO DE ÁREAS (M²)

Sala + cozinha integradas	17,39
Lavabo + lavanderia	3,85
Circulação	5,74
Suíte 1 (quarto)	7,84
Banho suíte 1	2,86
Suíte 2 (quarto)	9,81
Banho suíte 2	2,97
Área útil da casa	50,45
Garagem com pergolado (área aberta)	20,35
Área construída (casa, 4,00 × 14,50)	**58,00**
Taxa de ocupação · Coef. aproveitamento · Permeável	72,5% · 0,725 · 25,4%

QUADRO DE ESQUADRIAS

CÓD.	TIPO	L × H	PEIT.	QTD
P1	Porta de entrada, de giro	0,90 × 2,10	—	1
P2	Porta de giro	0,70 × 2,10	—	1
P3	Porta de giro	0,80 × 2,10	—	2
P4	Porta de giro	0,60 × 2,10	—	2
J1	Janela de correr	1,50 × 1,20	1,00	1
JS1	Janela alta basculante no shed 1	2,50 × 0,80	2,95	1
JS2	Janela alta basculante no shed 2	2,00 × 0,80	2,95	1
JS3	Janela alta basculante no shed 3	2,50 × 0,80	2,95	1
D1	Domus ventilado	0,80 × 0,80	teto	1
D2	Domus ventilado	0,60 × 0,60	teto	4
PG	Portão basculante ripado	2,70 × 2,20	—	1
PS	Portão social ripado	0,90 × 2,20	—	1

Pé-direito 2,70 m; forro inclinado sob os sheds. Paredes laterais e de fundo cegas (Código Civil, art. 1.301); janelas dos sheds perpendiculares às divisas e a mais de 0,75 m delas. Banheiros e lavabo com domus ventilado e exaustor. Verificar recuos, índices e aceitação dos sheds no código de obras do município.

PROJETO

Casa Térrea 4×20 — anteprojeto

LOTE	ÁREA CONSTRUÍDA
4,00 × 20,00 m (80,00 m²)	**58,00 m²**
ESCALA	DATA
1:100 (A3)	**nov/2026**

OBSERVAÇÃO

Estudo preliminar. Não substitui o projeto legal assinado por responsável técnico (RRT/ART).